


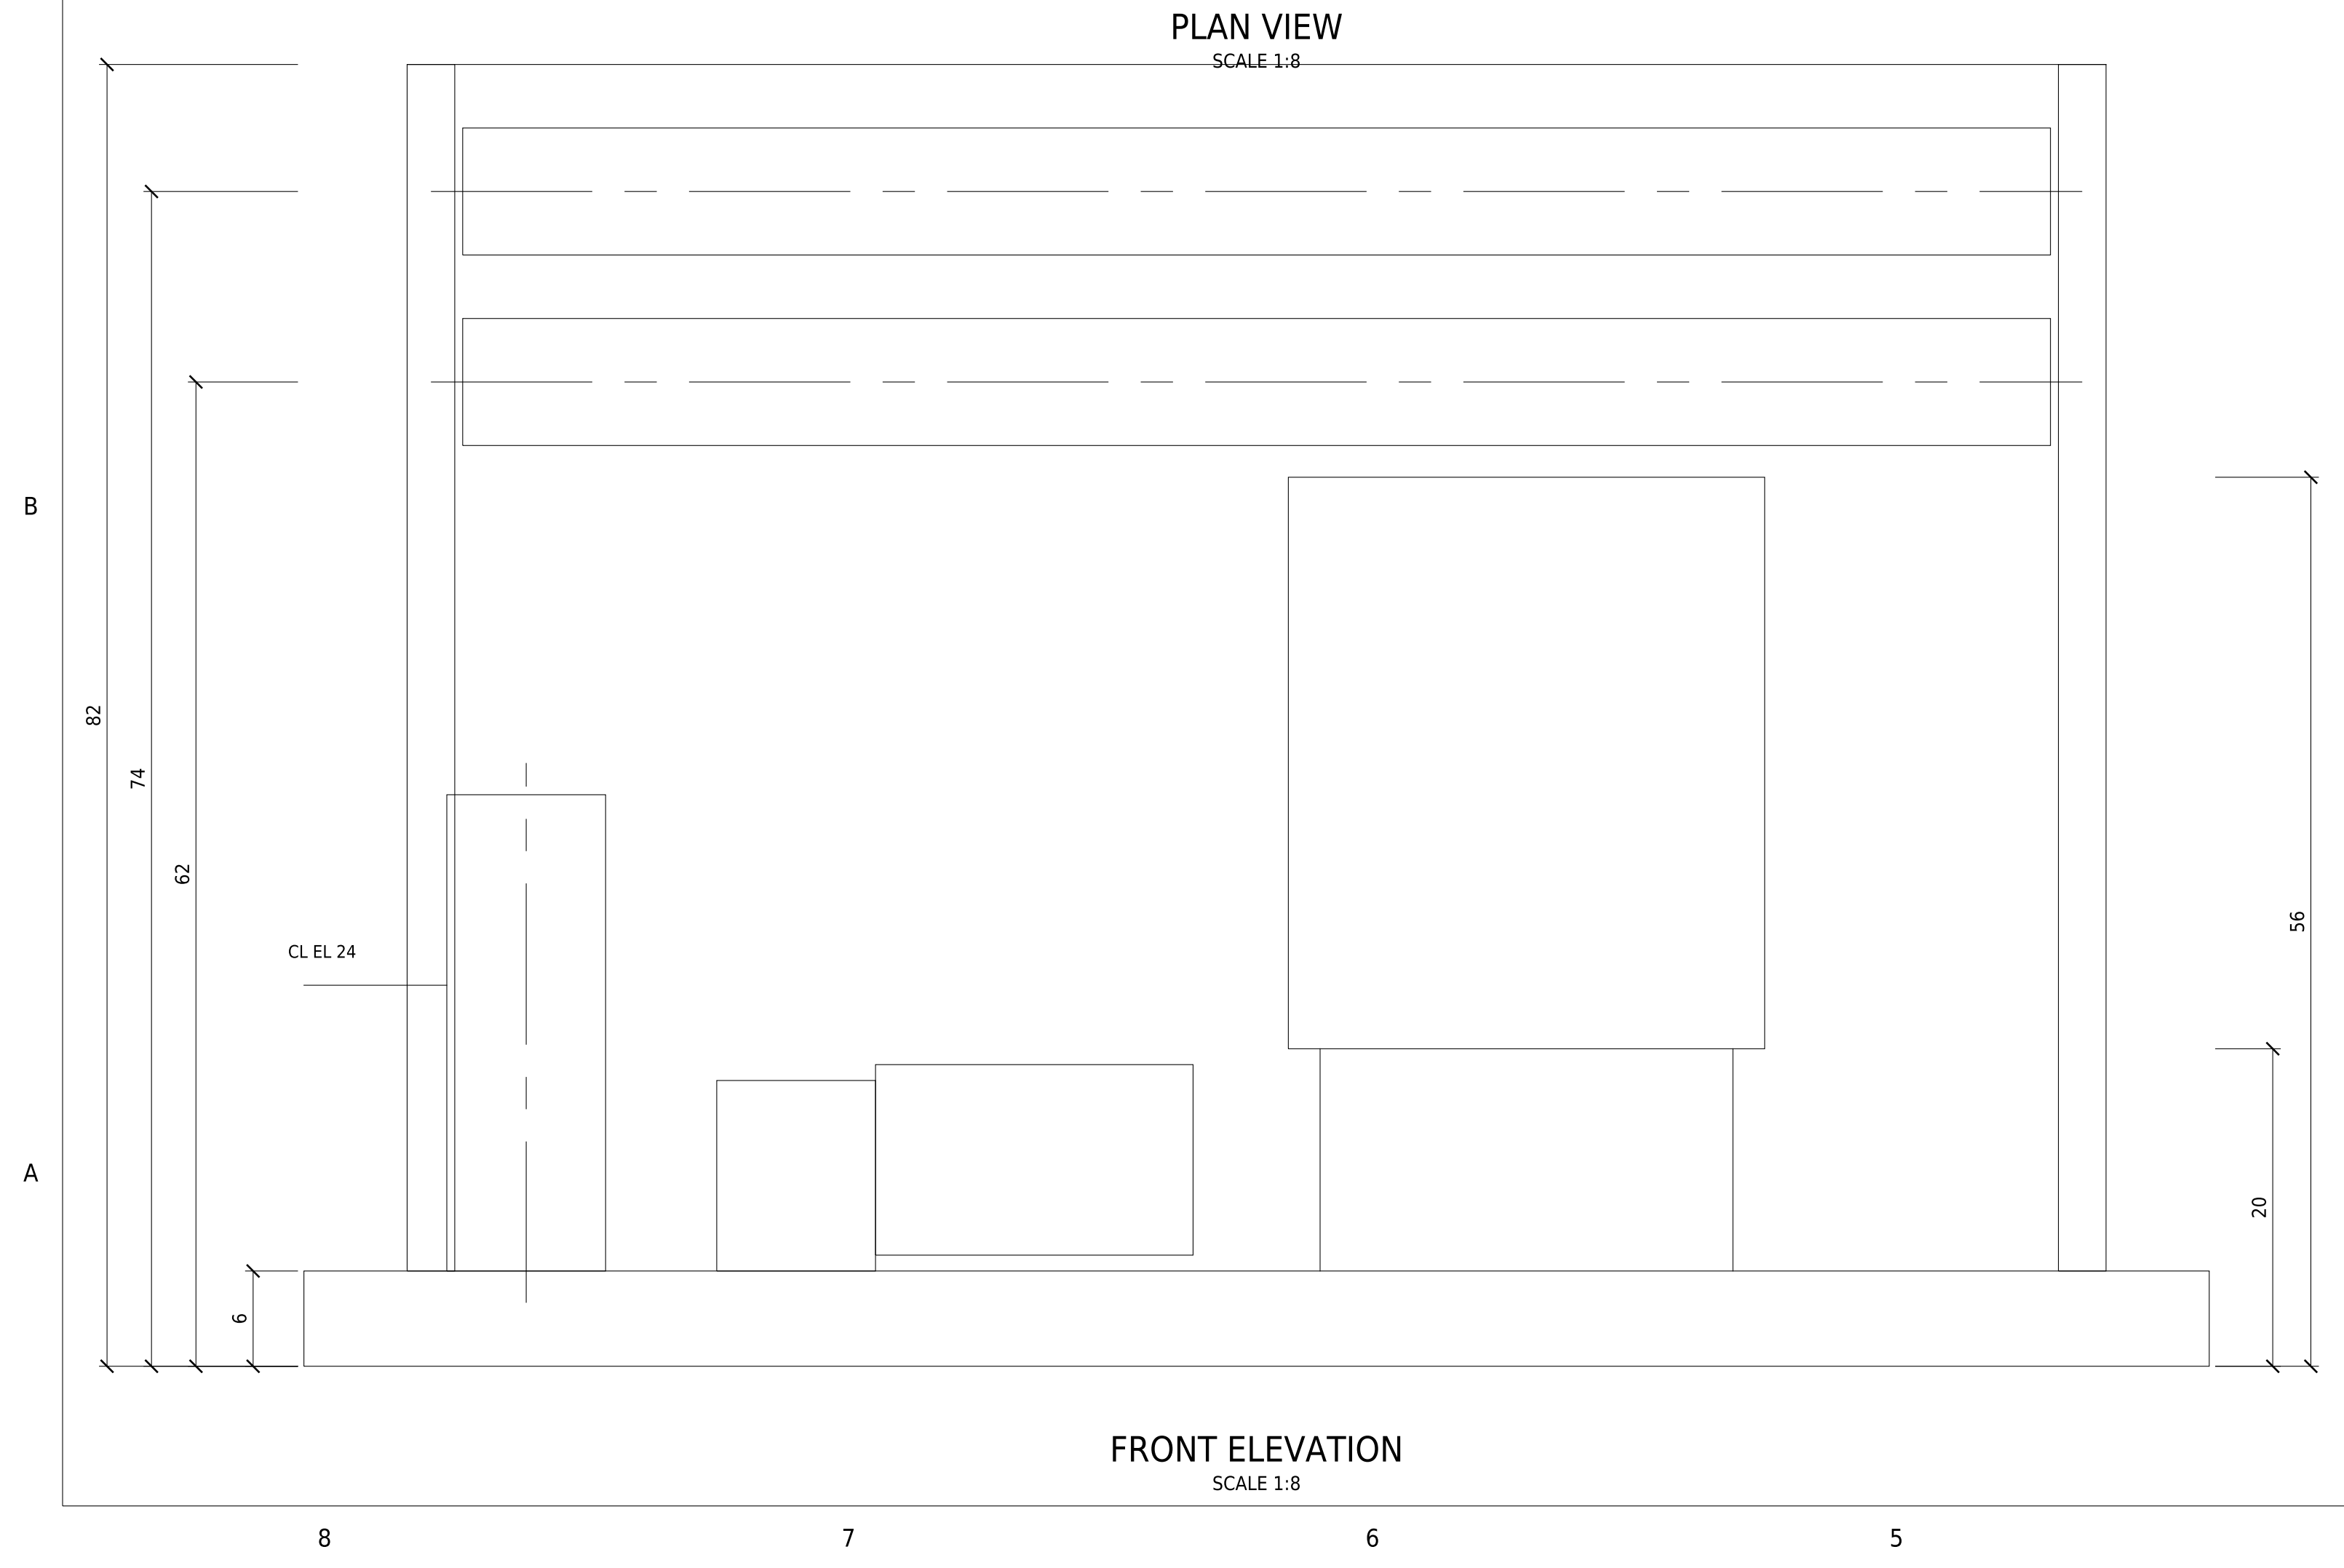


REVISIONS

1. ALL DIMENSIONS IN INCHES FROM DATUM A (FRAME CORNER) UNLESS NOTED.
2. LOW-PRESSURE PIPING: SCH 80 PVC. HIGH-PRESSURE PIPING: 316L SS.
3. FRAME: 304 SS C4X5.4, ALL WELDED. SEE DWG SMP-RO-110.
4. NOZZLE SIZES AND ORIENTATION PER P&ID SMP-PID-100 REV B.
5. VERIFY PUMP BASE HOLES AGAINST CERTIFIED VENDOR DRAWING.
6. DO NOT SCALE DRAWING.

NOZ	SERVICE	SIZE / RATING	CL EL
N1	FEED IN	1-1/2" 150# FLG	24
N2	PERMEATE OUT	1" 150# FLG	62
N3	CONCENTRATE OUT	3/4" NPT	62

ITEM	QTY	TAG	DESCRIPTION
1	1	CF-101	CARTRIDGE FILTER HOUSING, 5 MICRON, 20"
2	1	P-101	HIGH-PRESSURE PUMP, MULTISTAGE, 5 HP
3	2	PV-101/102	MEMBRANE PRESSURE VESSEL, 4" x 100", FRP
4	1	CP-101	CONTROL PANEL, NEMA 4X, 30x36x12
5	1	-	SKID FRAME, 120x48, 304 SS
6	1	-	PIPING, VALVES, INSTRUMENTS PER P&ID

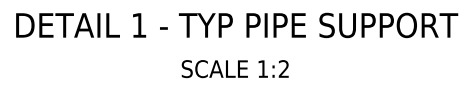

SAMPLE - PREPARED FOR PROPOSAL			
WATER TREATMENT SKID FABRICATION			
RO SKID - 10 GPM GENERAL ARRANGEMENT			
DWG NO. SMP-RO-100		REV B	
SCALE 1:8	DRAWN JEFF	CHECKED -	SHEET 1 OF 1